FRUCHTER HOUSE

원본 비례를 따라 다시 그린 평면 · 주요 관계 강조

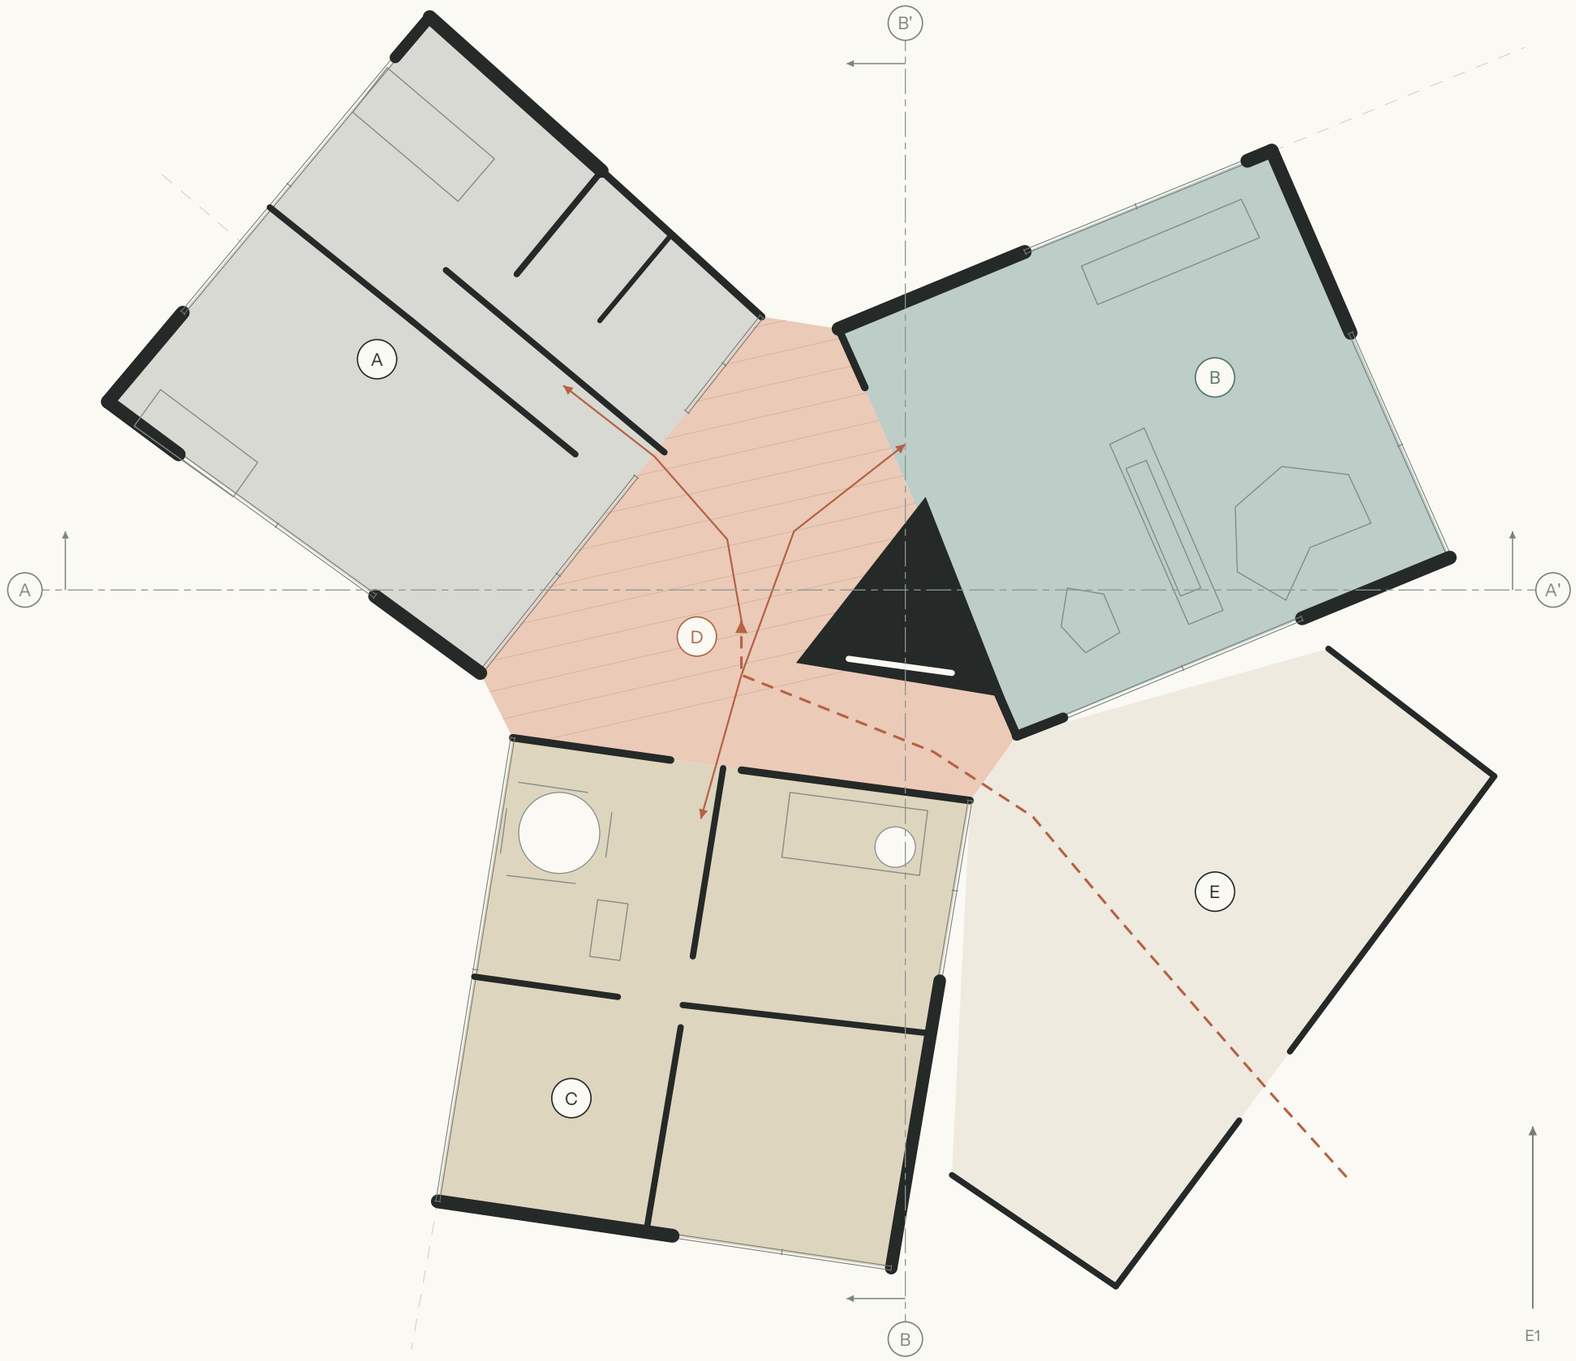

공간 읽기

A 개별실군

구획과 독립성 / 기능은 가설

B 공유실군

study corner · sitting

C 식사·서비스군

기구 기호 / 세부 실명 미확정

D 연결 중심

세 공간군을 잇는 불규칙한 여지

E 진입 마당

entrance court 표기

표현 기준
두꺼운 검정: 주요 경계와 중심 화로
얇은 회색: 내부 구획·가구·가벼운 외피
흙빛 점선: 제안한 진입 동선
A / B 절단선: 다음 장의 단면 위치

NTS / 실측 축척 없음
개구부의 정확한 폭·재료는 미확정
좌표와 높이는 해석용 모델의 가정

사용자 제공 스케치에 근거한 해석안. 원본 입면·단면 또는 시공 도면이 아님.

THE CONNECTIVE CENTRE

하나의 평면에서 투영한 입단면 · 높이와 지붕은 명시적 가설

A—A′ 세 공간의 연속

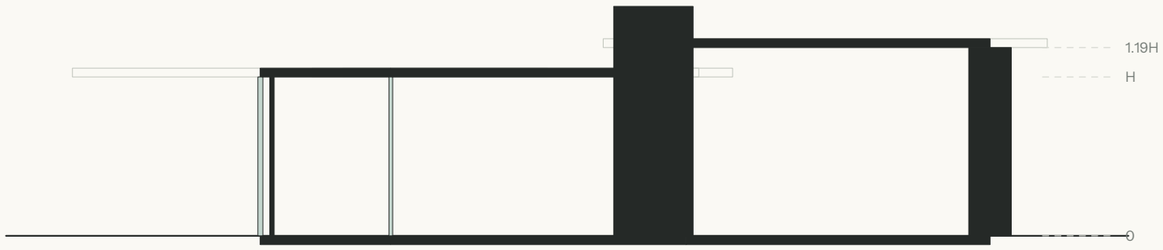

B—B′ 화로를 지나는 절단

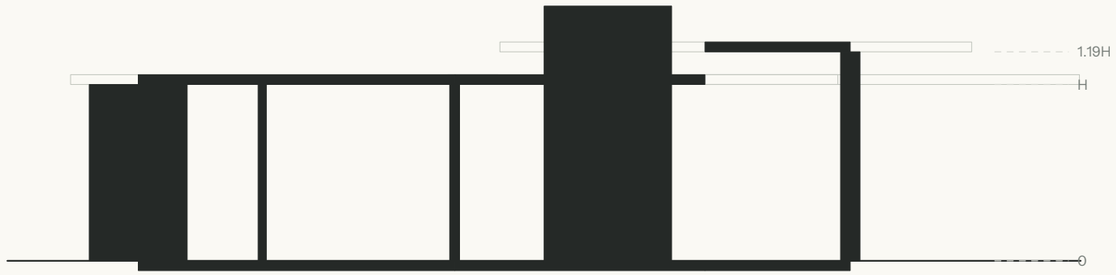

E1 진입 측 입면 가설

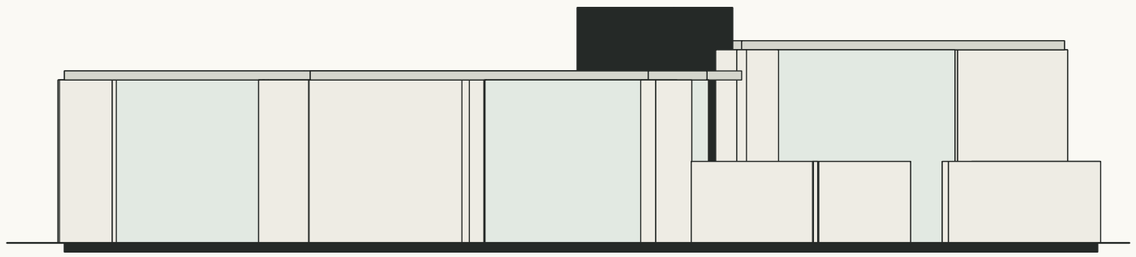

E1 | 진입 마당 쪽에서 본 입면 가설

가정한 상대 높이
개별실 · 서비스군 · 중앙 연결부: H
공유실: 1.19H / 화로 상부: 1.44H
진입 마당의 경계: 0.5H
지붕: 얇은 평지붕 / 중앙은 덮인 연결부

지붕을 들어 올린 관계 모형

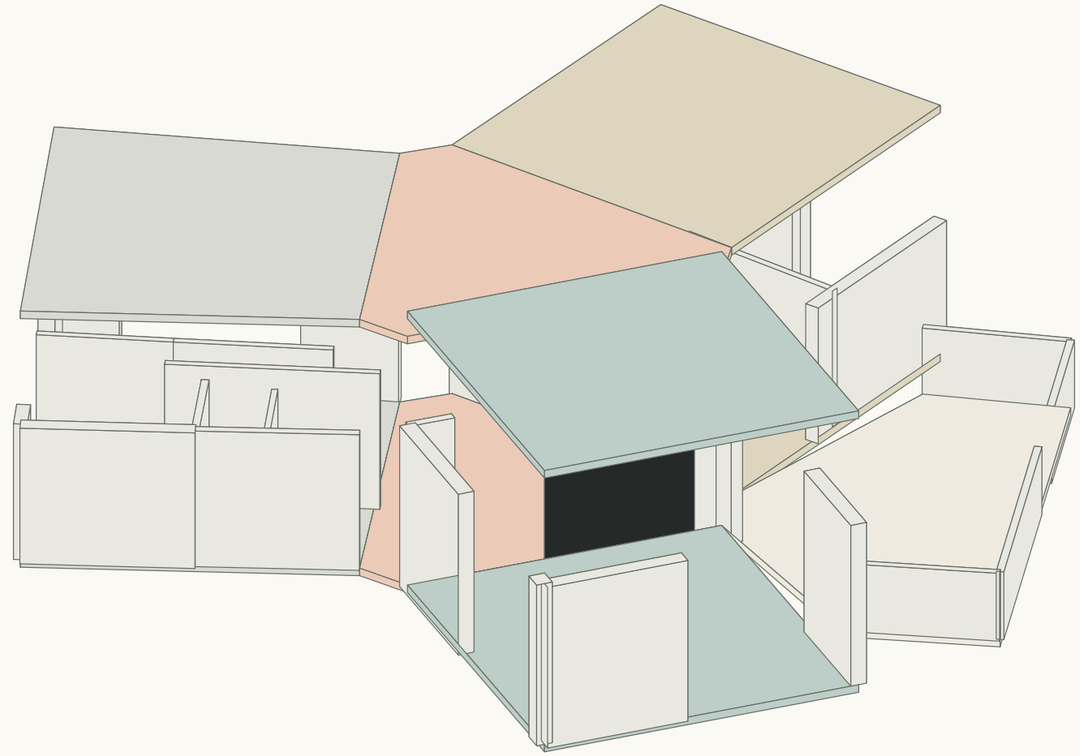

같은 좌표 모델에서 생성 / 지붕은 설명을 위해 위로 분리

주의: 모든 수직 구성은 제안이다. 원본만으로 실제 높이 · 지붕 · 창 위치를 확정할 수 없다.