
EXPAND / OVERLAP / CARVE

중앙의 모양을 바꾸기보다, 마주 보는 경계와 비우는 규칙을 바꾼다.

A 벌림 → 공동 중정

OUTWARD TRANSLATION / SAME ROTATION ANGLES

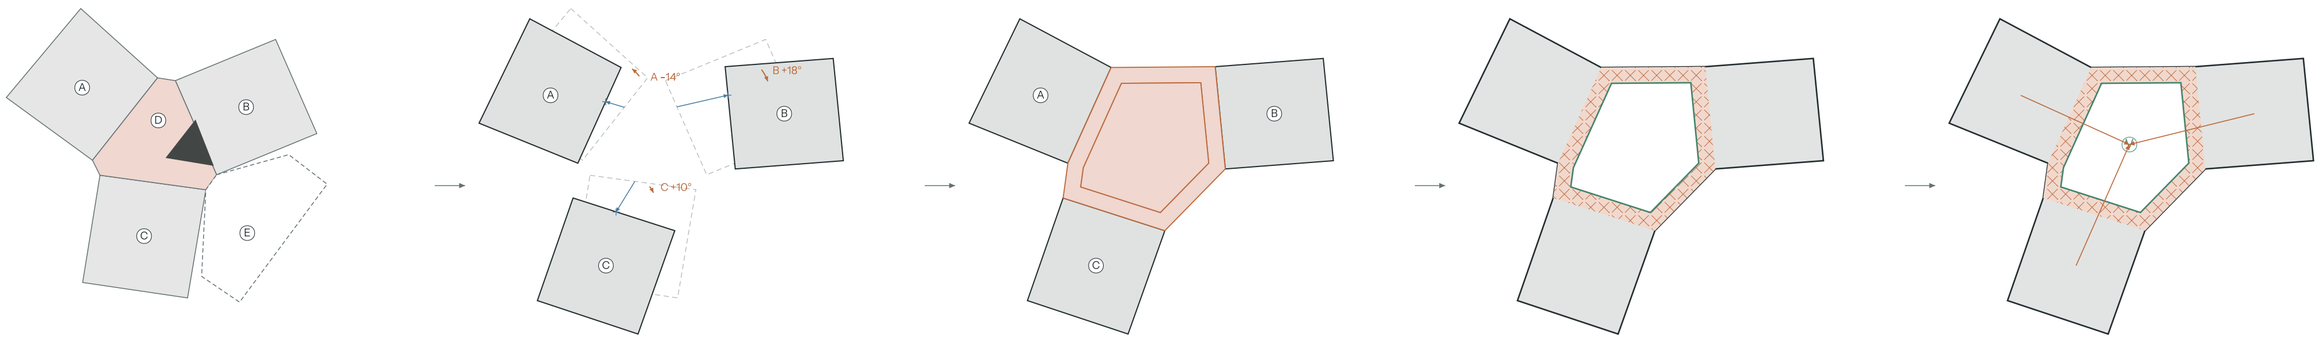

01 기존 관계 추출

A·B·C의 독립 방향, D의 연결, E의 진입을 기준으로 삼는다.

02 방향 + 거리 조정

A −14°, B +18°, C +10°. 바깥으로 이동시켜 마주 보는 거리를 늘린다.

03 사잇공간의 확대

서로 마주 보는 끝점을 연결한다. 잔여 틈을 공동 마당의 범위로 바꾼다.

04 가장자리 연결


확대한 틈의 안쪽을 비우고 둘레에 실내 연결 띠를 제안한다.

05 밖을 공유하는 중심

마당에 면한 세 경계가 새로운 정면이 된다. 큰 마당과 긴 이동이 함께 생긴다.

B 중첩 → 선택적 비움

INWARD TRANSLATION / ACTUAL FOOTPRINT INTERSECTION

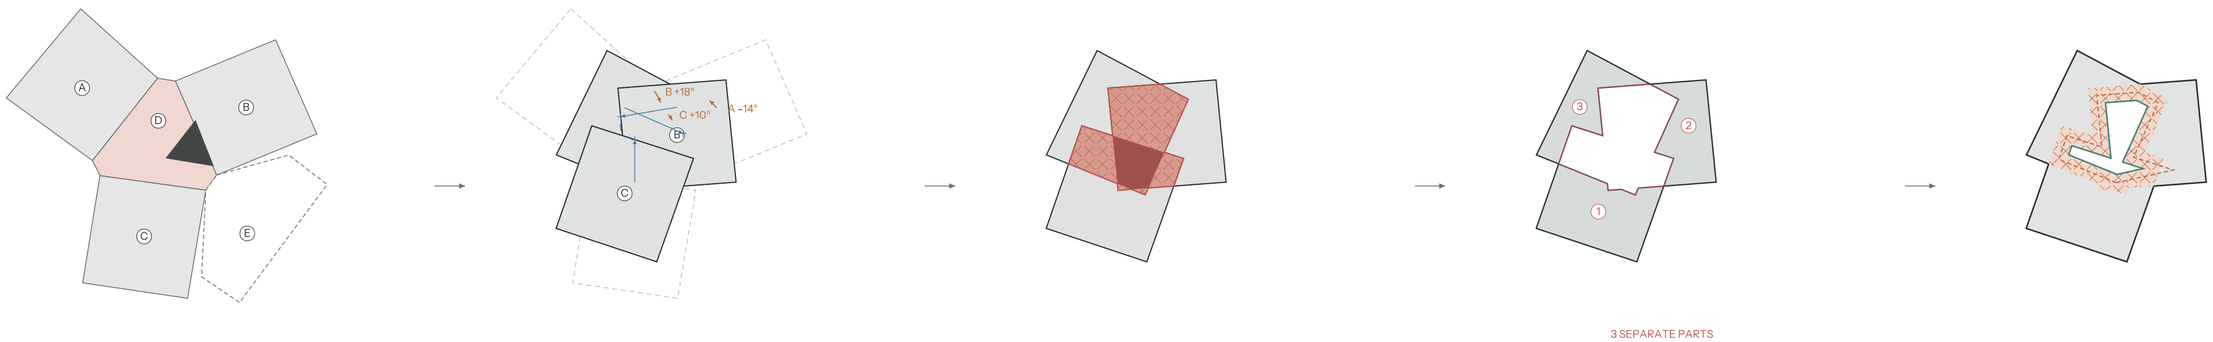

01 원형과의 관계 유지

가운데에 새 다각형을 먼저 그리지 않는다. 세 공간군의 경계에서 시작한다.

02 안으로 회전·이동

벌림안과 같은 각도, 다른 이동량. 안쪽 경계가 서로 겹치도록 배치한다.

03 중첩 면적 추출

O = (A∩B) ∪ (B∩C) ∪ (C∩A). 진한 면은 세 공간군의 공통 중첩이다.

04 전부 비우기: 보류

외곽에서 O 전체를 빼면 실내가 세 조각으로 분리된다. 연결 요구를 충족하지 못한다.

05 연결 띠를 남겨 비움

O의 가장자리는 실내 공유 공간으로 남긴다. 안쪽만 비워 연속된 바닥과 중정을 얻는다.

기존 공간군의 변형

실제 중첩 영역

실내 공유 공간

중정: 하늘에 열린 비움

두 줄의 모든 평면은 같은 상대 축척·도면 방향이다. 회전각은 설계 가설이며, A/B는 이동량도 다른 대안 비교다. 점선은 원래 외곽 또는 순환 동선으로 각 단계에서 구분한다.

0 1 U


U = 기존 A 안쪽 변 길이. 실측 축척·방위 미확인 / 원본의 삼각형 요소는 출처 참조이며 새 용도를 확정하지 않음.

TWO COURTS / DIFFERENT CONSEQUENCES

넓히는 중정과 겹쳐 비우는 중정은, 같은 빈 공간이지만 다른 관계를 만든다.


A / EXPANDED COURT

바깥의 공동 마당 + 둘레의 실내 연결

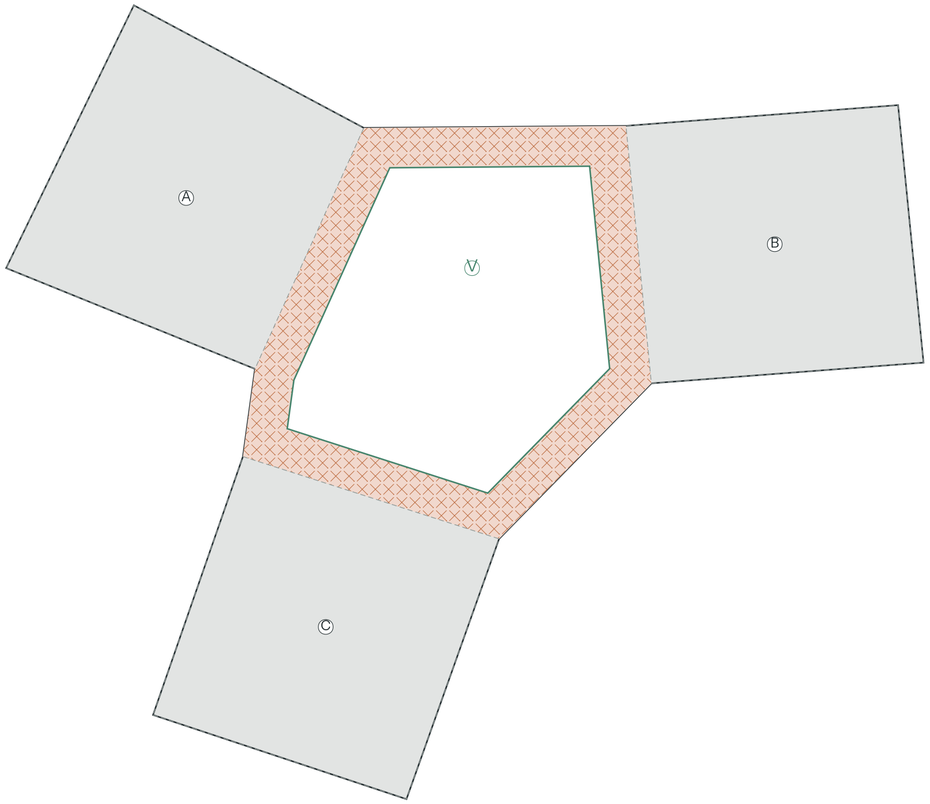

B / SELECTIVE SUBTRACTION

안쪽의 빛마당 + 연결을 유지하는 실내 띠

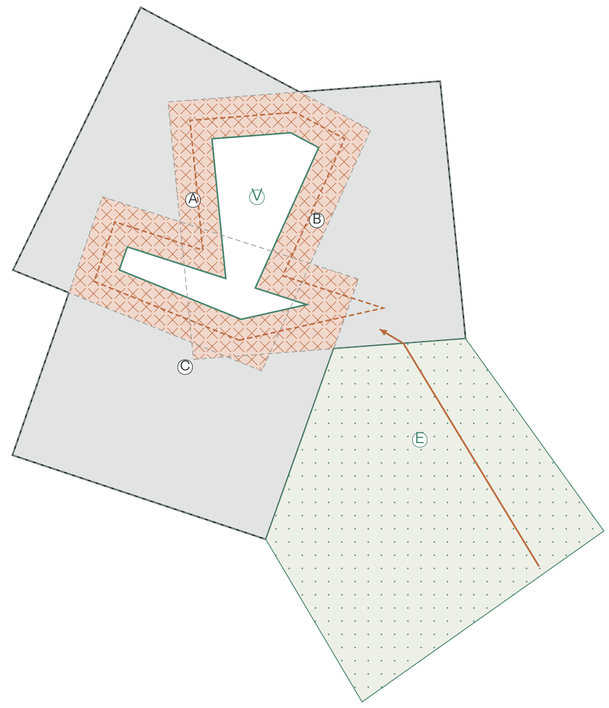

선정: 도서관·공유작업소의 연결된 실내를 우선

독립된 방향은 남기되 경계 일부를 공유한다. 중정은 채광·시선의 중심, 실내 띠는 이동·만남의 중심이다. 외부 E는 큰 모임을 받아 안쪽 중정의 과밀을 줄인다.

0 — 1U

동일한 상대 축척 / 외곽선 기준 비교


비교 항목	A 벌림	B 선택적 비움
실내 외곽 면적 / 원래 세 공간군 면적 합	122.4% / 3.810 U^2	63.2% / 1.969 U^2
하늘에 열린 안쪽 마당	1.104 U^2	0.218 U^2
실내 공유 띠 / 바닥의 연속성	0.697 U^2 / 연결됨	0.541 U^2 / 연결됨
얻는 것 / 치르는 비용	큰 공동 마당 / 외곽 확장·긴 이동	가까운 접점·연속 실내 / 사용 면적 감소

면적은 벽 두께를 공제하지 않은 도형 면적. 대지·법규·실측 면적 미확인으로 수용 인원이나 성능 우열을 확정하지 않는다.

판단 기준: 내부 연결·조용한 열람·외부 모임의 분리. A를 폐기하지 않고 비교 대안으로 유지한다.

READ / MEET / MAKE

도서관·공유작업소: 바깥의 넓은 마당과 안쪽의 비워진 빛마당을 함께 쓴다.

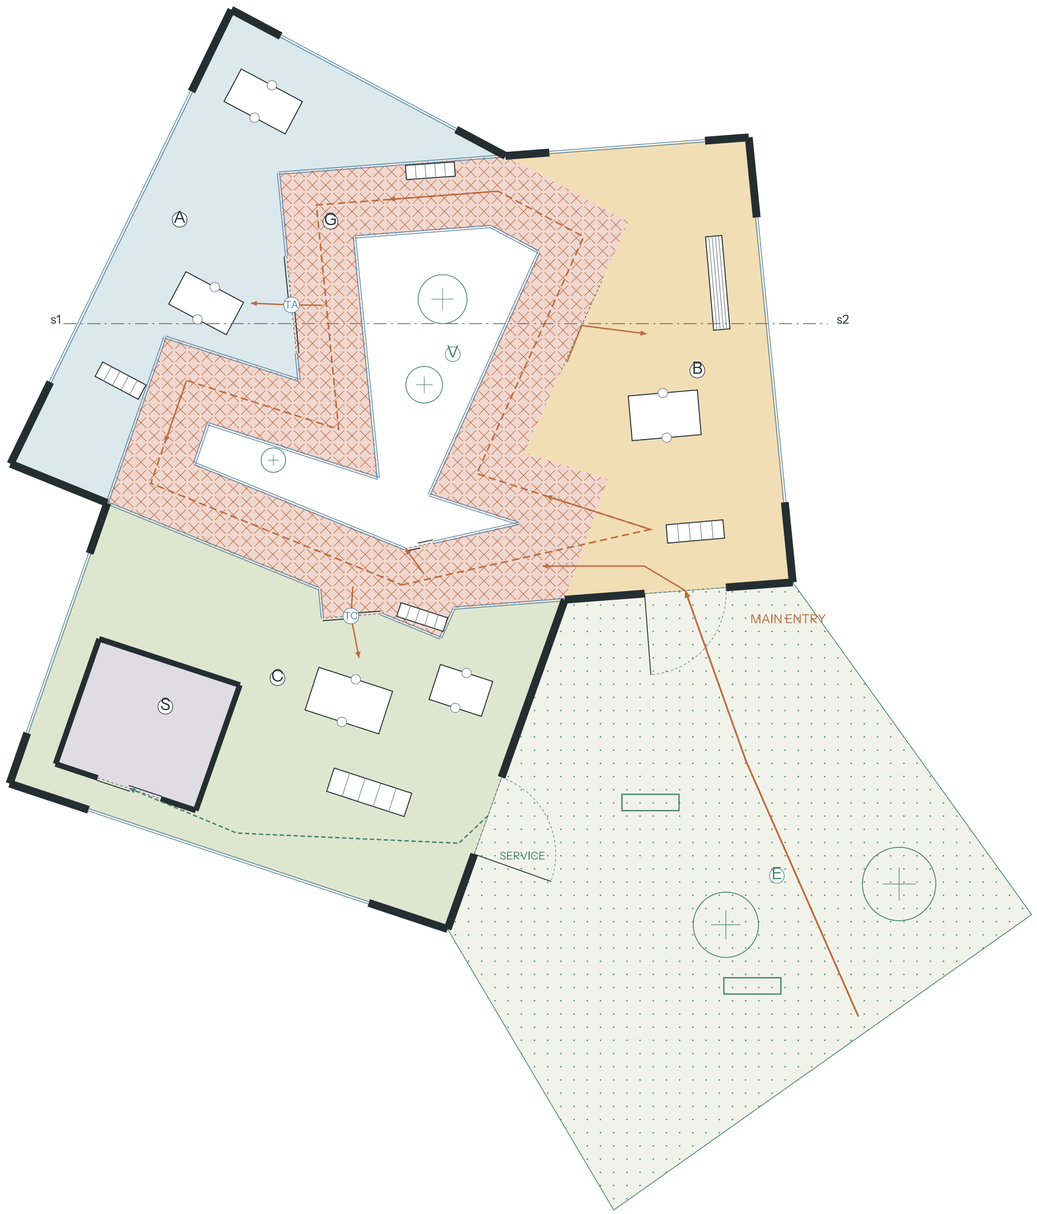

선과 면의 역할

벽체 — 유리 경계 — 순환·진입 — 단면·참조

0 — 1U

도면 내 1 U = 105.41 mm / 실측 축척 아님

경계가 프로그램을 만든다

A 조용한 열람·학습

유리 경계와 문턱 TA로 공유 공간의 소리를 조절한다.

B 열린 서가·모임

주진입에 가까운 열린 접점. 안내·가벼운 대화가 먼저 온다.

C 공유작업·자료 보수

별도 운영 출입과 문턱 TC. 소음·분진이 큰 제작은 제외한다.

G 실내 공유 갤러리

북측은 앉아 읽기, 남측은 작은 전시. 그 옆으로 순환 동선을 잇는다.


V / E 빛마당 / 진입 마당

V는 채광·식재·짧은 체류, E는 모임·야외 교류를 받는다.

S 위생·운영 공간 유보

필수 설비를 위한 영역만 확보했다. 실측 규모가 정해지기 전에는 위생기구·수용 인원·피난 적합성을 확정하지 않는다.

s1–s2 개념 단면 / 평면 절단선과 대응

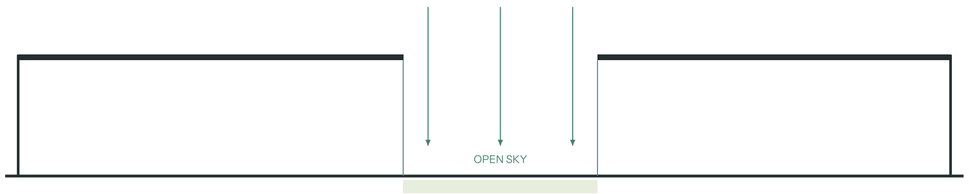

A / 열람 — B / 서가

수평 경계는 평면에서 추출. 높이·구조·지붕 구성은 미확정.

왜 도서관·공유작업소인가

조용한 열람, 열린 대화, 가벼운 제작을 분리하면서도 자료와 활동을 공유할 수 있다. 중정은 통행량의 중심이 아니라 서로의 활동을 보게 하는 중심이다.

병원은 청결·환자·운영 동선 분리가 더 엄격하고, 학교는 교실 규모와 피난 조건, 시장은 물류·위생 요구가 크다. 현재의 작은 공간군 실험에는 도서관형 조합이 우선 적합하다.

TA·TC·중정·S: 미닫이 제안 / 띠 기준 폭 0.152 U, 유효 폭 미검증.

설계 제안 평면. 벽·가구·유리·출입문은 새 가설 / 실내 바닥과 중정의 분리, 동선 중심선·가구 충돌을 기하 검토.